




VISTA FRONTAL
ESC. 1:5

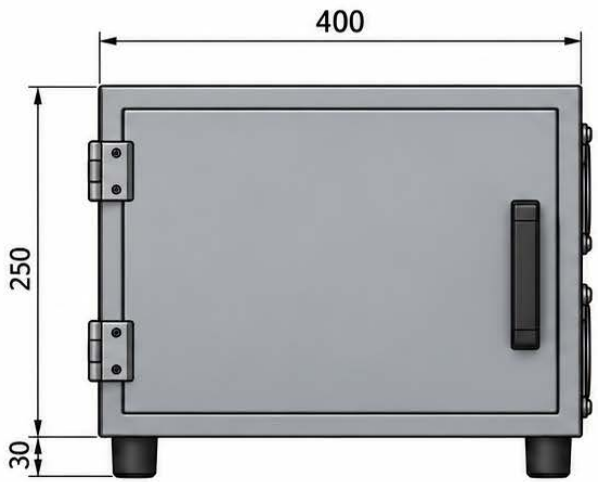


VISTA LATERAL DERECHA
ESC. 1:5

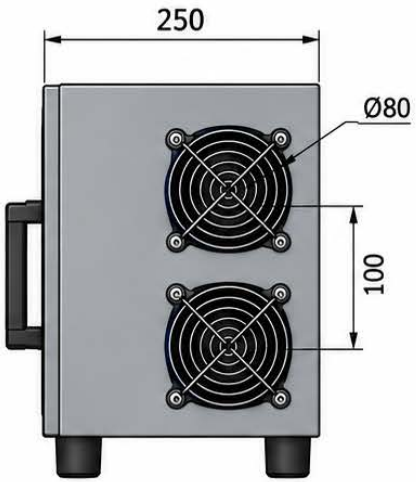

VISTA ISOMÉTRICA
ESC. 1:5

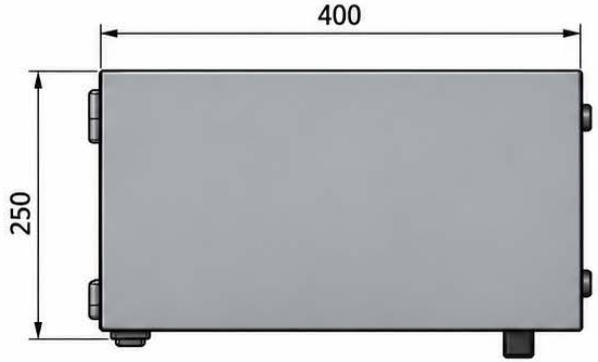

VISTA SUPERIOR
ESC. 1:5

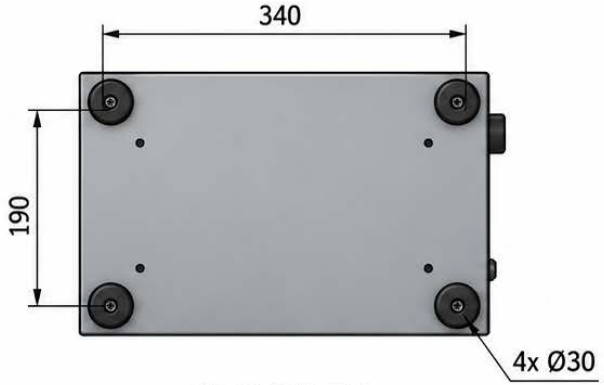

VISTA INFERIOR
ESC. 1:5

REV.	FECHA	DESCRIPCIÓN	DIS. REV.	APROBADO	NÚMERO DE PLANOS	REFERENCIAS DE PLANOS

KOVATI E.I.R.L.
KOVATI E.I.R.L.
A.H Pedro P. Diaz Mz. 4B Lt. 23,
Cerro Colorado, Arequipa, Perú
Teléfono: (054) 627-184
Correo: proyectos@kovati.com

CONFIDENCIAL
ESTE PLANO Y LA INFORMACION CONTENIDA EN EL SON PROPIEDAD DE KOVATI E.I.R.L.
SU USO Y REPRODUCCION SIN AUTORIZACION PREVIA, ESTAN PROHIBIDOS.

NUMERO DE PLANO ORIGINAL
15315-2600-46DD-300

FECHA
07.SET.2026

APROBADO	07.SET.2026	
DISEÑADO POR:	L. CHURA	FECHA: 07.SET.2026
DIBUJADO POR:	L. CHURA	FECHA: 07.SET.2026
REVISADO POR:	J. CERRON	FECHA: 07.SET.2026
APROBADO POR:	J. CERRON	FECHA: 07.SET.2026
CLIENTE:	A. COSAITI	FECHA: 07.SET.2026

TECSUP
Arequipa - Perú


PAD B – FASE 1
INGENIERIA DE DETALLE

PLANO
HORNO ELÉCTRICO – VISTAS GENERALES


ESCALA: S/E

NUMERO DE PLANO: A1-MI09H060-260-70-121

REV.: 0

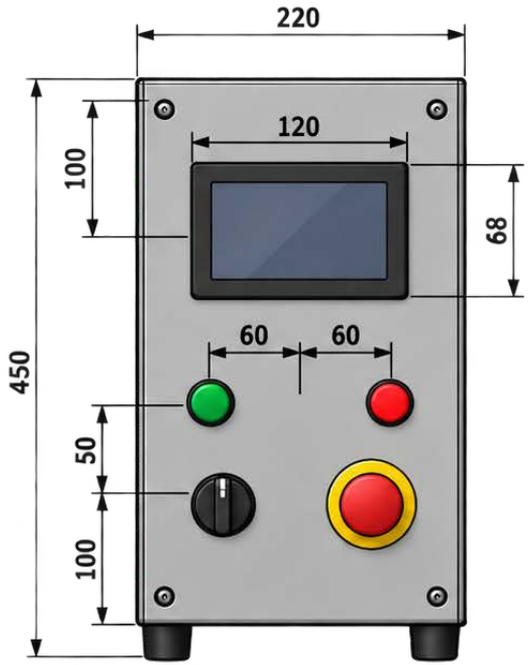


VISTA FRONTAL
ESCALA 1:5

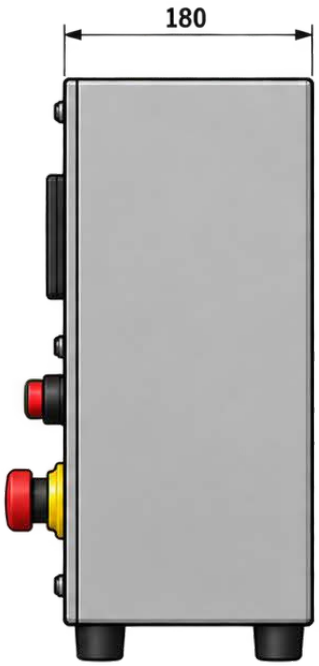

VISTA LATERAL DERECHA
ESCALA 1:5



VISTA ISOMÉTRICA
ESCALA 1:5

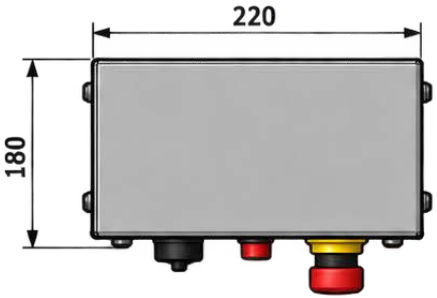

VISTA SUPERIOR
ESCALA 1:5

REV.	FECHA	DESCRIPCIÓN	DIS. REV.	APROBADO	NÚMERO DE PLANOS	REFERENCIAS DE PLANOS

KOVATI E.I.R.L.
KOVATI E.I.R.L.
A.H Pedro P. Diaz Mz. 48 Lt. 23,
Cerro Colorado, Arequipa, Perú
Teléfono: (054) 627-184
Correo: proyectos@kovati.com

CONFIDENCIAL
ESTE PLANO Y LA INFORMACION CONTENIDA EN EL SON PROPIEDAD DE KOVATI E.I.R.L.
SU USO Y REPRODUCCION SIN AUTORIZACION PREVIA, ESTAN PROHIBIDOS.

NUMERO DE PLANO ORIGINAL: 15315-2600-46DD-300

FECHA: 07.SET.2026

APROBADO	07.SET.2026	
DISEÑADO POR:	L. CHURA	FECHA: 07.SET.2026
DIBUJADO POR:	L. CHURA	FECHA: 07.SET.2026
REVISADO POR:	J. CERRON	FECHA: 07.SET.2026
APROBADO POR:	J. CERRON	FECHA: 07.SET.2026
CLIENTE:	A. COSAITI	FECHA: 07.SET.2026

TECSUP
Arequipa - Perú


PAD B – FASE 1
INGENIERIA DE DETALLE

PLANO
TABLERO DE CONTROL - VISTAS GENERALES

ESCALA: S/E

NUMERO DE PLANO: A1-MI09H060-260-70-121

REV.: 0

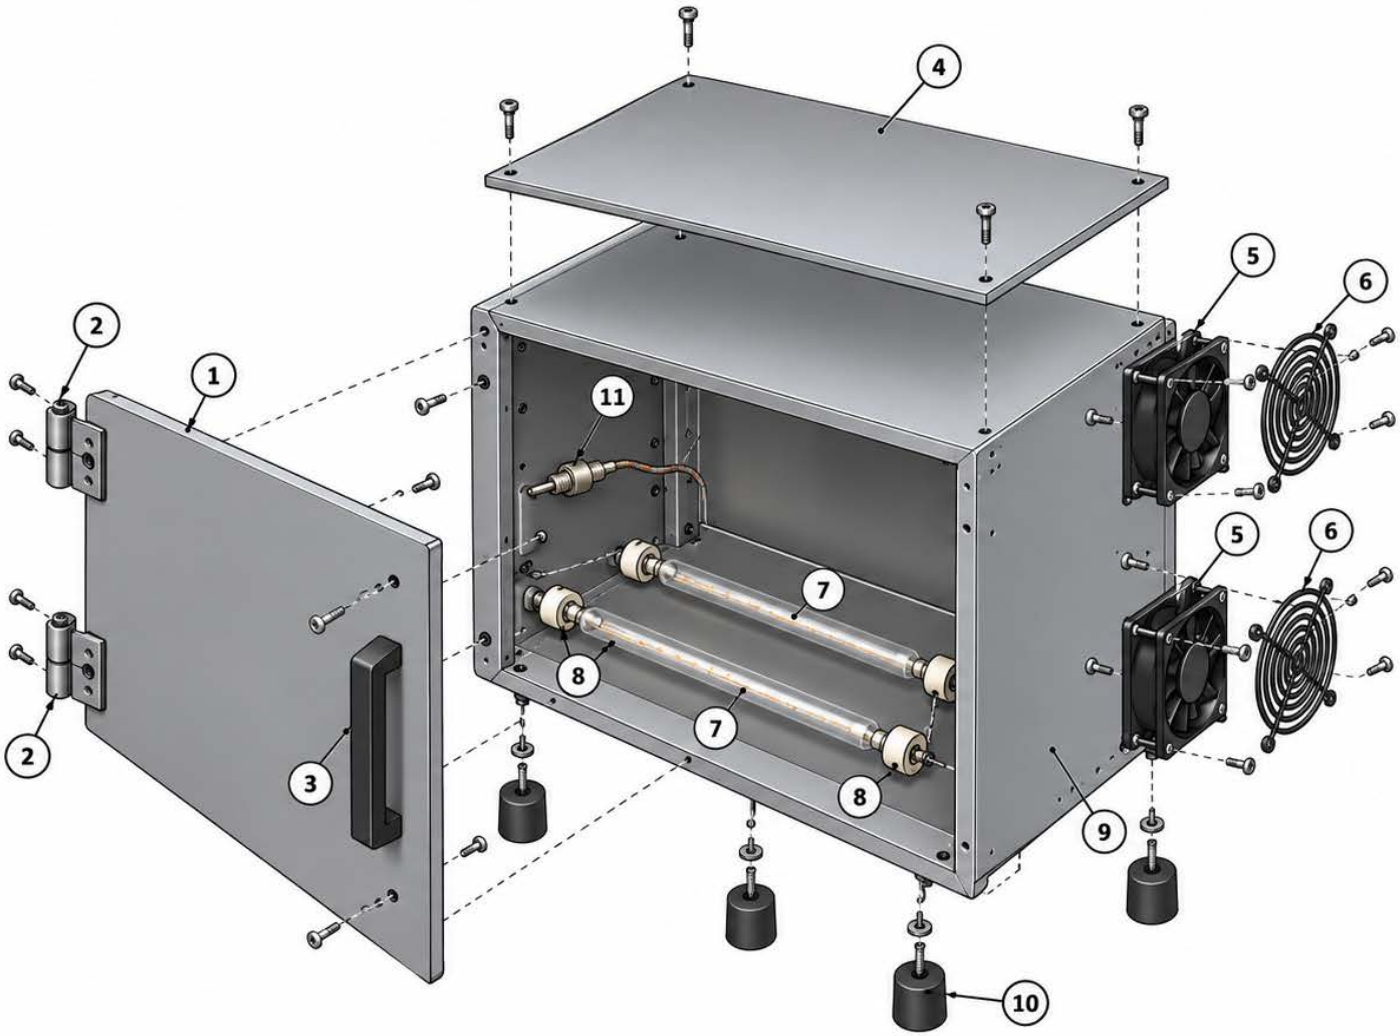

N.°	DESCRIPCIÓN	CANT.
1	Puerta frontal	1
2	Bisagra	2
3	Manija de puerta	1
4	Tapa superior	1
5	Ventilador lateral	2
6	Rejilla de ventilador	2
7	Lámpara halógena tubular	2
8	Portalámpara cerámico	4
9	Caja del horno (acero galvanizado)	1
10	Pie de goma	4
11	Sensor de temperatura RTD Pt100	1
12	Tornillería de fijación	16

REV.	FECHA	DESCRIPCIÓN	DIS. / REV.	APROBADO	NÚMERO DE PLANOS	REFERENCIAS DE PLANOS

KOVATI E.I.R.L.
KOVATI E.I.R.L.
A.H Pedro P. Díaz Mz. 48 Lt. 23,
Cerro Colorado, Arequipa, Perú
Teléfono: (054) 627-184
Correo: proyectos@kovati.com

CONFIDENCIAL
ESTE PLANO Y LA INFORMACIÓN CONTENIDA EN EL SON PROPIEDAD DE KOVATI E.I.R.L.
SU USO Y REPRODUCCIÓN SIN AUTORIZACIÓN PREVIA, ESTÁN PROHIBIDOS.

NUMERO DE PLANO ORIGINAL: 15315-2600-46DD-300

FECHA: 07.SET.2026

APROBADO	07.SET.2026	
DISEÑADO POR:	L. CHURA	FECHA: 07.SET.2026
DIBUJADO POR:	L. CHURA	FECHA: 07.SET.2026
REVISADO POR:	J. CERRON	FECHA: 07.SET.2026
APROBADO POR:	J. CERRON	FECHA: 07.SET.2026
CLIENTE:	A. COSAITI	FECHA: 07.SET.2026

TECSUP
Arequipa - Perú


PAD B – FASE 1
INGENIERÍA DE DETALLE

PLANO
ESTRUCTURA MECÁNCA DEL HORNO – PLANO DE DESPIECE

ESCALA: S/E

NUMERO DE PLANO: A1-MI09H060-260-70-121

REV.: 0

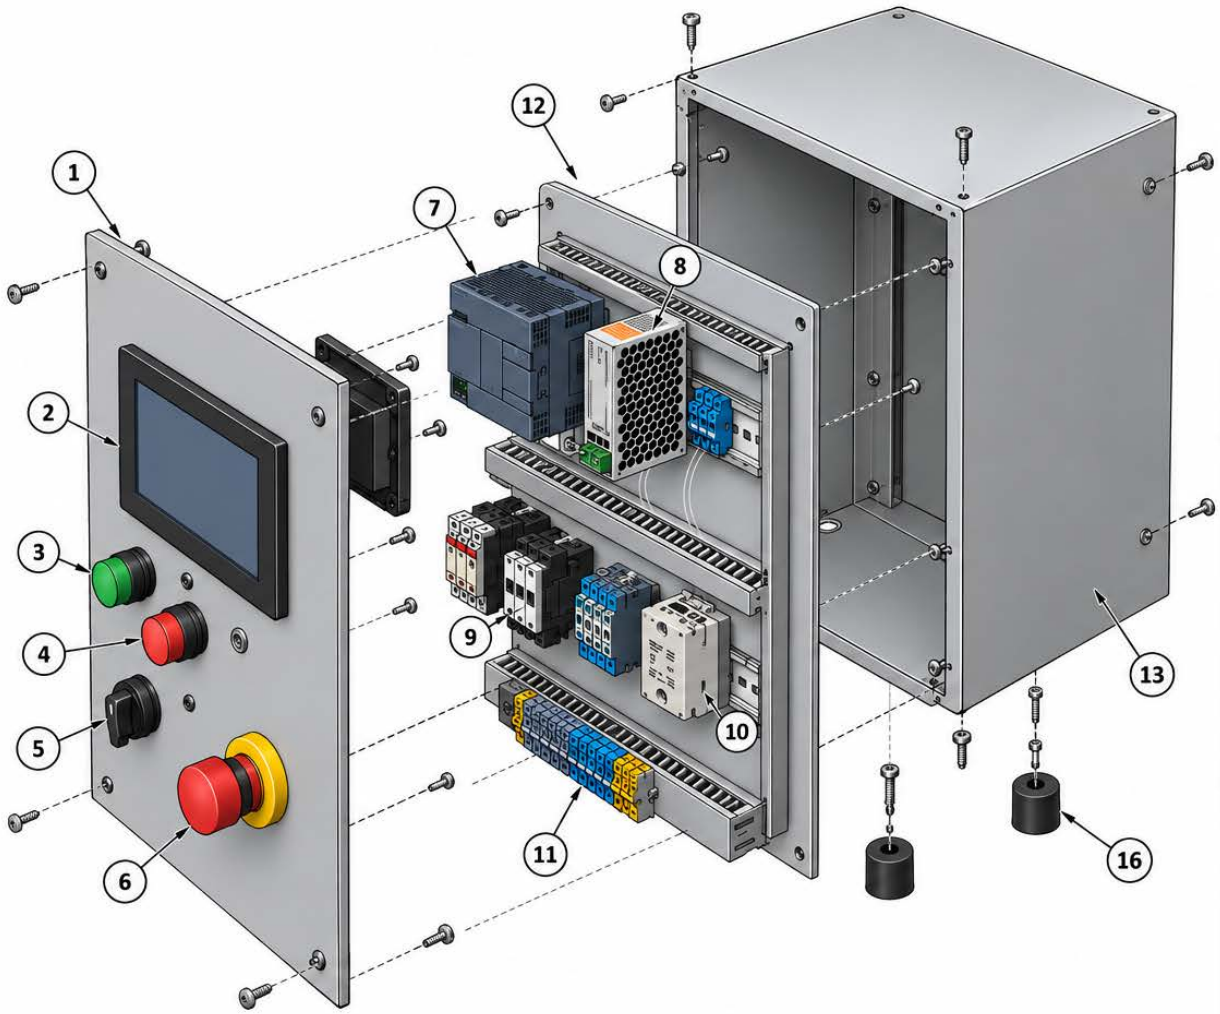

N.°	DESCRIPCIÓN	CANT.
1	Tapa frontal	1
2	HMI Siemens KTP700	1
3	Pulsador de marcha (verde)	1
4	Pulsador de parada (rojo)	1
5	Selector ON/OFF	1
6	Pulsador de emergencia	1
7	PLC Siemens S7-1200 CPU 1212C DC/DC/DC	1
8	Fuente de alimentación 220 VAC / 24 VDC	1
9	Contactor de seguridad	1
10	Regulador de potencia (SSR)	1
11	Borneras	1
12	Placa de montaje (riel DIN + canaletas)	1
13	Caja del tablero (chapa metálica)	1
16	Pies de goma	4

REV.	FECHA	DESCRIPCIÓN	DIS. REV.	APROBADO	NÚMERO DE PLANOS	REFERENCIAS DE PLANOS

KOVATI E.I.R.L.
KOVATI E.I.R.L.
Av. Pedro P. Díaz Mz. 48 Lt. 23,
Cerro Colorado, Arequipa, Perú
Teléfono: (054) 627-184
Correo: proyectos@kovati.com

CONFIDENCIAL
ESTE PLANO Y LA INFORMACIÓN CONTENIDA EN EL SON PROPIEDAD DE KOVATI E.I.R.L.
SU USO Y REPRODUCCIÓN SIN AUTORIZACIÓN PREVIA, ESTÁN PROHIBIDOS.

NUMERO DE PLANO ORIGINAL: 15315-2600-46DD-300

FECHA: 07.SET.2026

APROBADO	07.SET.2026	
DISEÑADO POR:	L. CHURA	FECHA: 07.SET.2026
DIBUJADO POR:	L. CHURA	FECHA: 07.SET.2026
REVISADO POR:	J. CERRON	FECHA: 07.SET.2026
APROBADO POR:	J. CERRON	FECHA: 07.SET.2026
CLIENTE:	A. COSAITI	FECHA: 07.SET.2026

TECSUP
Arequipa - Perú

PAD B – FASE 1
INGENIERIA DE DETALLE

PLANO
TABLERO DE CONTROL – PLANO DE DESPIECE

ESCALA: S/E

NUMERO DE PLANO: A1-MI09H060-260-70-121

REV.: 0