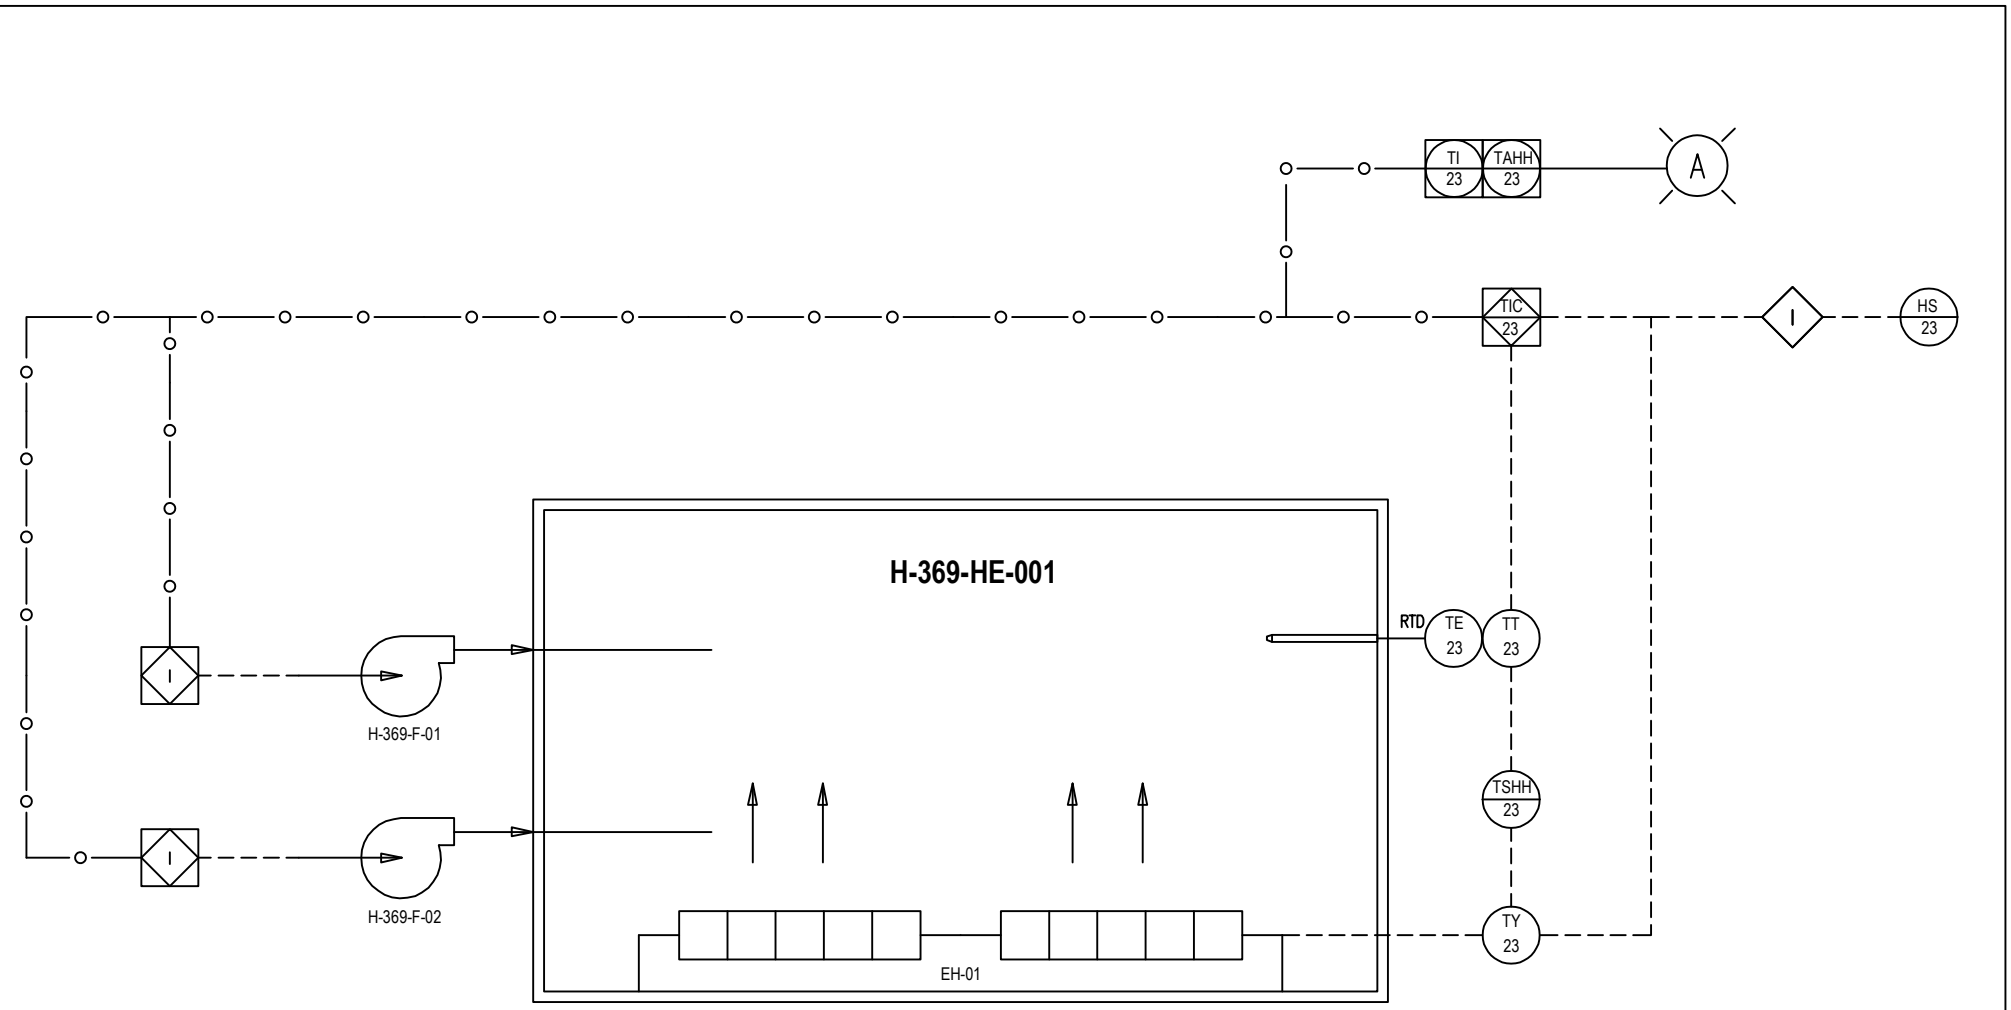


REV.	FECHA	DESCRIPCIÓN	DIS. / REV.	APROBADO	NÚMERO DE PLANOS	REFERENCIAS DE PLANOS
A		EMITIDO PARA COORDINACIÓN INTERNA	S.R / J.C			

KOVATI E.I.R.L.
KOVATI E.I.R.L.
Av. Pedro P. Diaz Mz. 4B Lt. 23,
Cerro Colorado, Arequipa, Perú
Teléfono: (054) 627-184
Correo: proyectos@kovati.com

CONFIDENCIAL
ESTE PLANO Y LA INFORMACION CONTENIDA EN EL SON PROPIEDAD DE KOVATI E.I.R.L.
SU USO Y REPRODUCCION SIN AUTORIZACION PREVIA, ESTAN PROHIBIDOS.

NUMERO DE PLANO ORIGINAL: 15315-2600-46DD-300

FECHA: 07.SET.2026

APROBADO	07.SET.2026	
DISEÑADO POR:	S. ROMERO	FECHA: 07.SET.2026
DIBUJADO POR:	S. ROMERO	FECHA: 07.SET.2026
REVISADO POR:	J. CERRON	FECHA: 07.SET.2026
APROBADO POR:	J. CERRON	FECHA: 07.SET.2026
CLIENTE:	A. COSAITI	FECHA: 07.SET.2026

TECSUP
Arequipa - Perú

PAD B – FASE 1
INGENIERIA DE DETALLE

PLANO
PLANO P&ID HORNO ELÉCTICO PARA CURADO DE BARNIZ

ESCALA: S/E

NUMERO DE PLANO: A1-MI09H060-260-70-011

REV.: 0