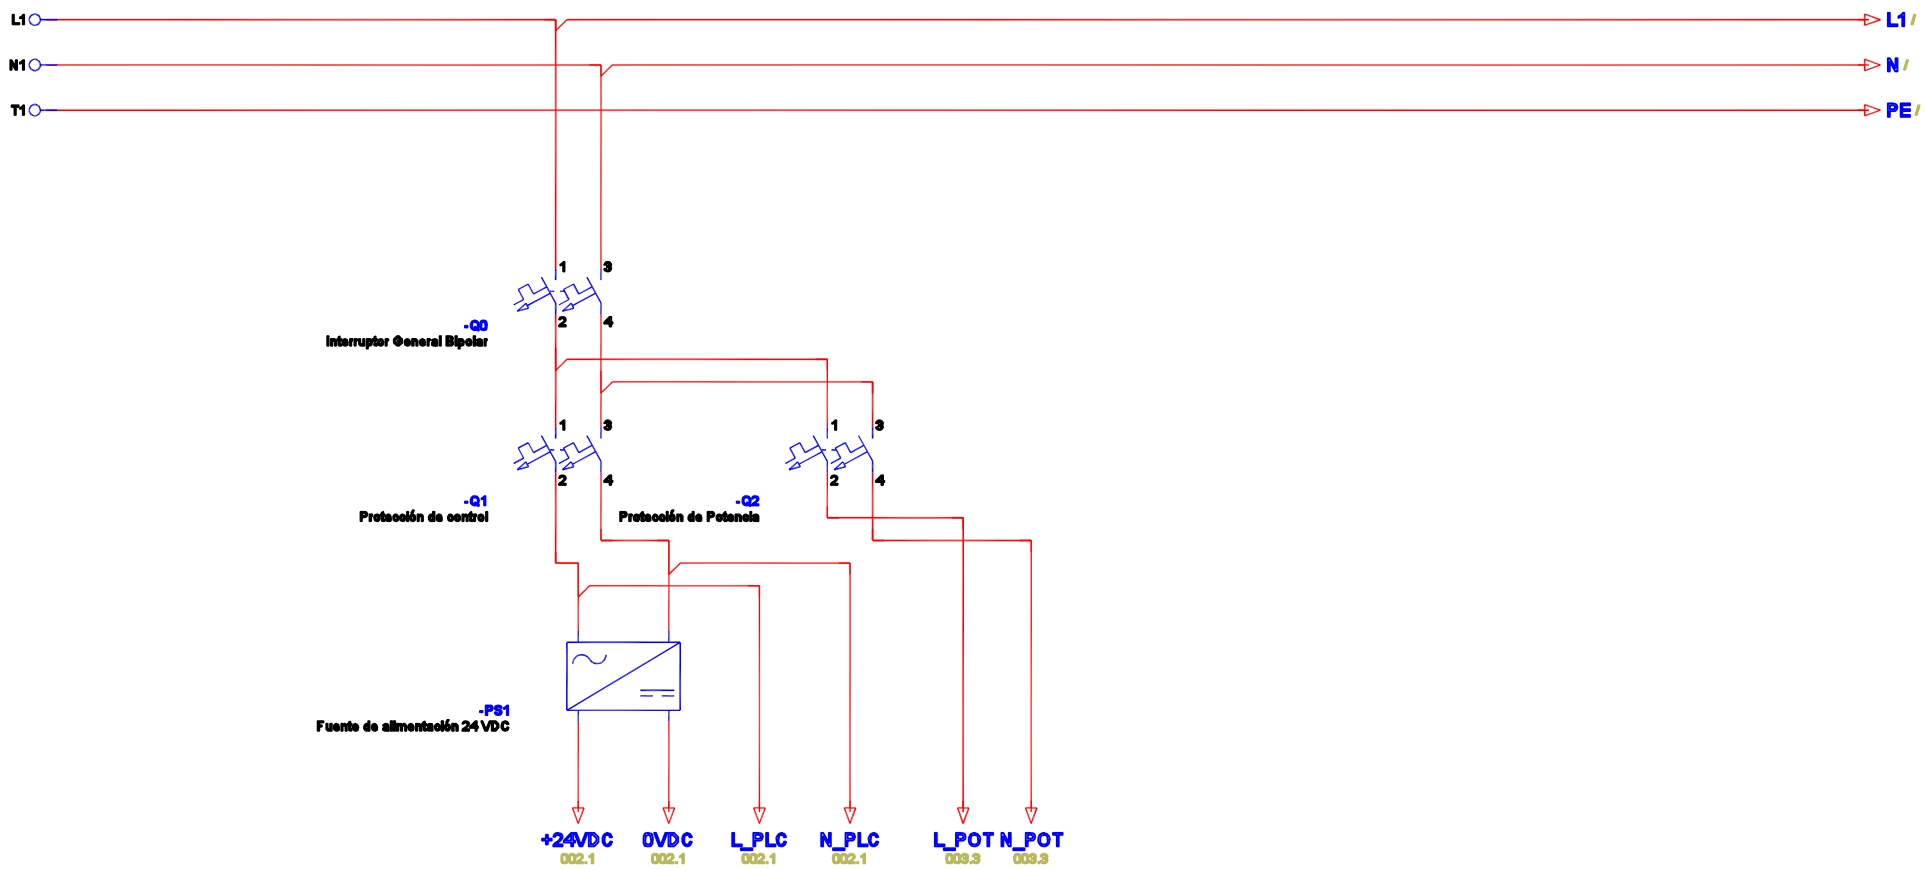


REV.	FECHA	DESCRIPCIÓN	DIS. REV.	APROBADO	NÚMERO DE PLANOS	REFERENCIAS DE PLANOS

KOVATI E.I.R.L.
A.H Pedro P. Diaz Mz. 4B Lt. 23,
Cerro Colorado, Arequipa, Perú
Teléfono: (054) 627-184
Correo: proyectos@kovati.com

CONFIDENCIAL
ESTE PLANO Y LA INFORMACION CONTENIDA EN EL SON PROPIEDAD DE KOVATI E.I.R.L.
SU USO Y REPRODUCCION SIN AUTORIZACION PREVIA, ESTAN PROHIBIDOS.

NUMERO DE PLANO ORIGINAL
15315-2600-46DD-300

FECHA
07.SET.2026

APROBADO	07.SET.2026	
DISEÑADO POR:	R. PACCO	FECHA: 07.SET.2026
DIBUJADO POR:	R. PACCO	FECHA: 07.SET.2026
REVISADO POR:	J. CERRON	FECHA: 07.SET.2026
APROBADO POR:	J. CERRON	FECHA: 07.SET.2026
CLIENTE:	A. COSAITI	FECHA: 07.SET.2026

TECSUP
Arequipa - Perú


PAD B – FASE 1
INGENIERIA DE DETALLE

PLANO
DIAGRAMA ELÉCTRICO DE DISTRIBUCIÓN DE ALIMENTACIÓN

ESCALA: S/E

NUMERO DE PLANO: A1-MI09H060-260-70-120

REV.: 0

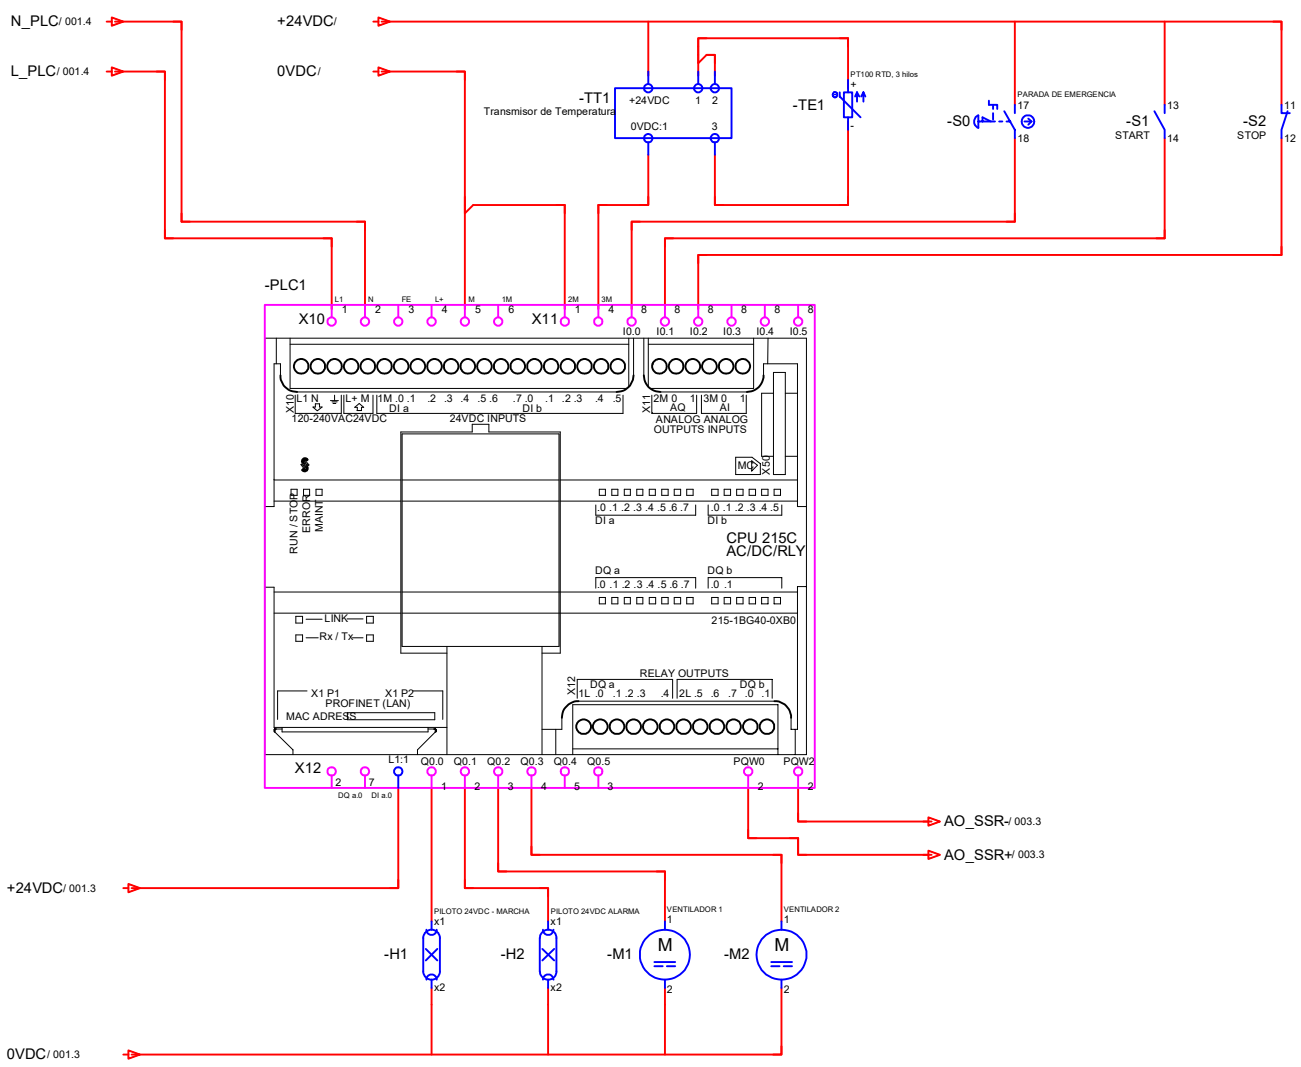

REV.	FECHA	DESCRIPCIÓN	DIS. REV.	APROBADO	NÚMERO DE PLANOS	REFERENCIAS DE PLANOS

KOVATI E.I.R.L.
Av. Pedro P. Diaz Mz. 4B Lt. 23,
Cerro Colorado, Arequipa, Perú
Teléfono: (054) 627-184
Correo: proyectos@kovati.com

CONFIDENCIAL
ESTE PLANO Y LA INFORMACION CONTENIDA EN EL SON PROPIEDAD DE KOVATI E.I.R.L.
SU USO Y REPRODUCCION SIN AUTORIZACION PREVIA, ESTAN PROHIBIDOS.

NUMERO DE PLANO ORIGINAL: 15315-2600-46DD-300

FECHA: 07.SET.2026

APROBADO	07.SET.2026	
DISEÑADO POR:	R. PACCO	FECHA: 07.SET.2026
DIBUJADO POR:	R. PACCO	FECHA: 07.SET.2026
REVISADO POR:	J. CERRON	FECHA: 07.SET.2026
APROBADO POR:	J. CERRON	FECHA: 07.SET.2026
CLIENTE:	A. COSAITI	FECHA: 07.SET.2026

TECSUP
Arequipa - Perú


PAD B – FASE 1
INGENIERIA DE DETALLE

PLANO
DIAGRAMA ELÉCTRICO DE CONEXIONES DEL PLC S7-1200

ESCALA: S/E

NUMERO DE PLANO: A1-MI09H060-260-70-110

REV.: 0

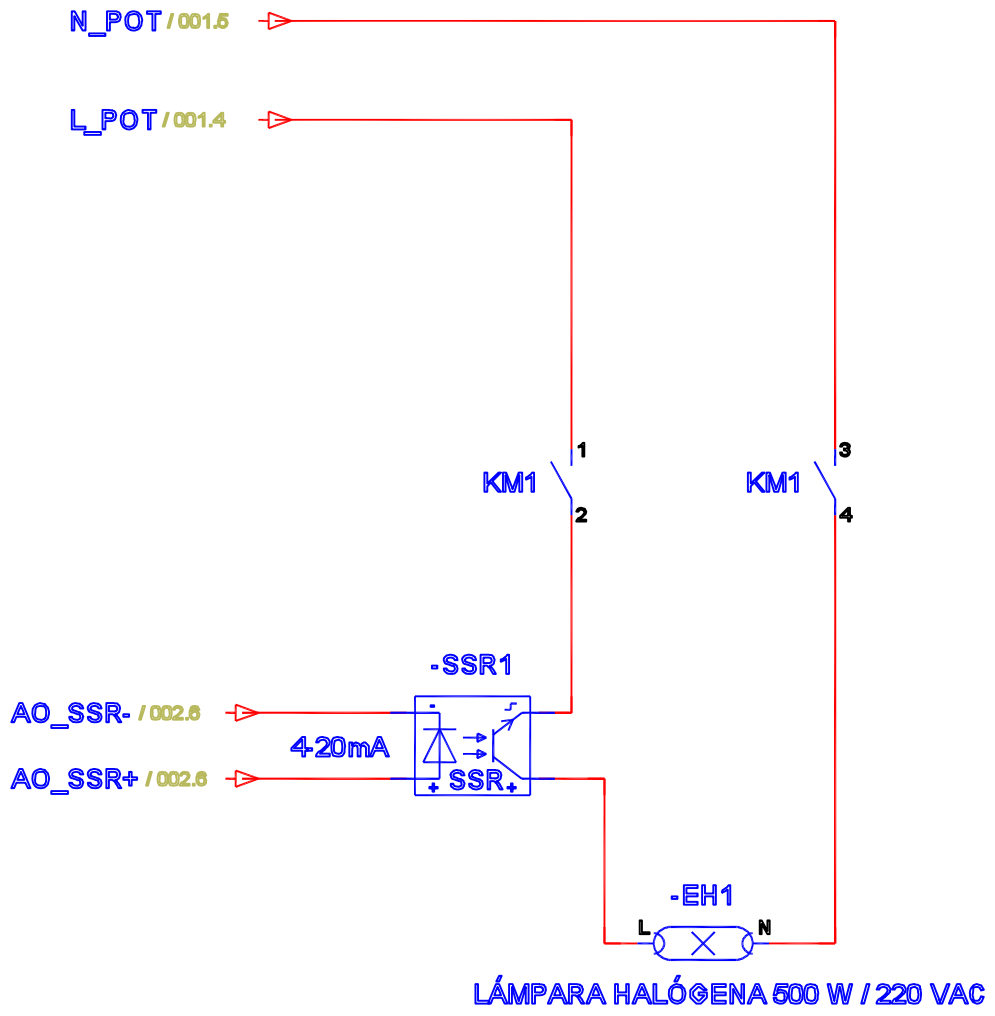

REV.	FECHA	DESCRIPCIÓN	DIS. REV.	APROBADO	NÚMERO DE PLANOS	REFERENCIAS DE PLANOS

KOVATI E.I.R.L.
KOVATI E.I.R.L.
A.H Pedro P. Diaz Mz. 48 Lt. 23,
Cerro Colorado, Arequipa, Perú
Teléfono: (054) 627-184
Correo: proyectos@kovati.com

CONFIDENCIAL
ESTE PLANO Y LA INFORMACION CONTENIDA EN EL SON PROPIEDAD DE KOVATI E.I.R.L.
SU USO Y REPRODUCCION SIN AUTORIZACION PREVIA, ESTAN PROHIBIDOS.

NUMERO DE PLANO ORIGINAL: 15315-2600-46DD-300

FECHA: 07.SET.2026

APROBADO	07.SET.2026	
DISEÑADO POR: R. PACCO	FECHA:	07.SET.2026
DIBUJADO POR: R. PACCO	FECHA:	07.SET.2026
REVISADO POR: J. CERRON	FECHA:	07.SET.2026
APROBADO POR: J. CERRON	FECHA:	07.SET.2026
CLIENTE: A. COSAITI	FECHA:	07.SET.2026

TECSUP
Arequipa - Perú


PAD B – FASE 1
INGENIERIA DE DETALLE

PLANO
DIAGRAMA ELÉCTRICO DE POTENCIA Y CONTROL DE CALEFACCIÓN

ESCALA: S/E

NUMERO DE PLANO: A1-MI09H060-260-70-121

REV.: 0

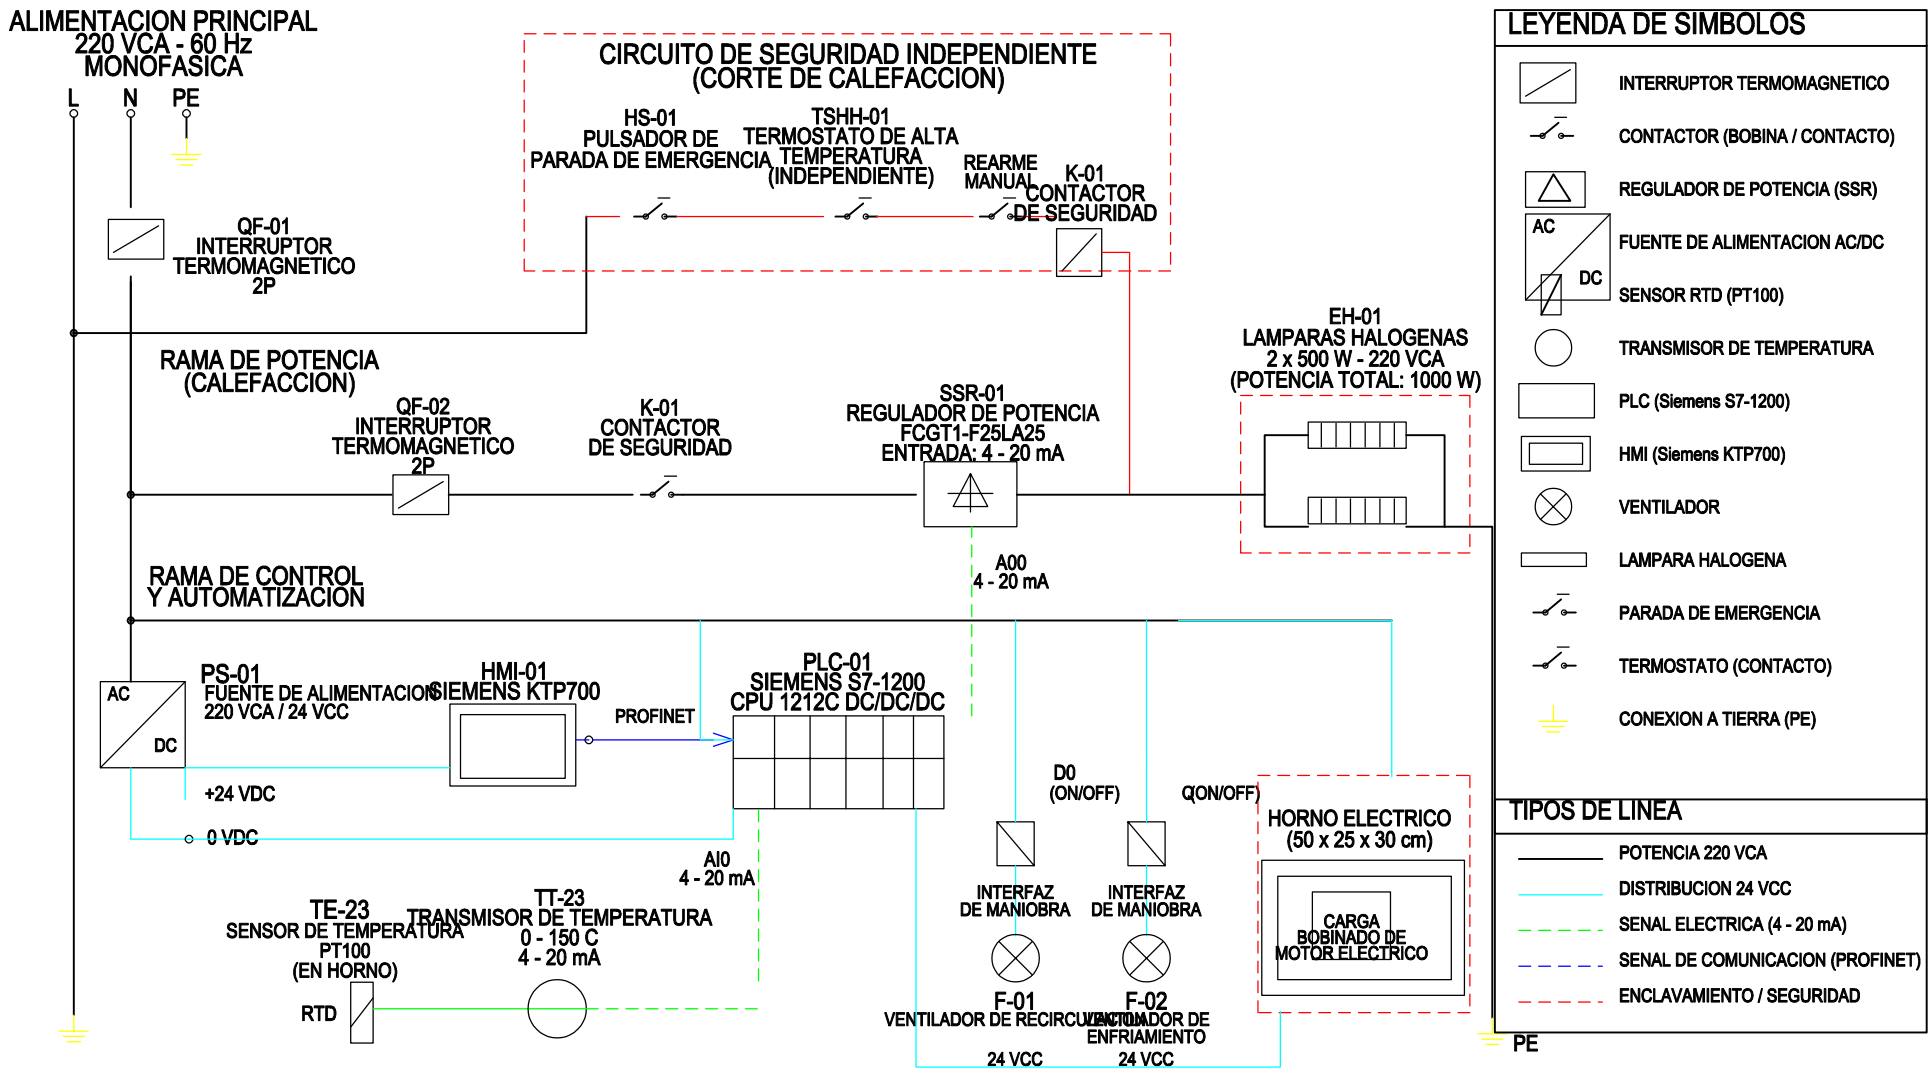

REV.	FECHA	DESCRIPCIÓN	DIS. REV.	APROBADO	NÚMERO DE PLANOS	REFERENCIAS DE PLANOS

KOVATI E.I.R.L.
Av. Pedro P. Diaz Mz. 48 Lt. 23,
Cerro Colorado, Arequipa, Perú
Teléfono: (054) 627-184
Correo: proyectos@kovati.com

CONFIDENCIAL
ESTE PLANO Y LA INFORMACION CONTENIDA EN EL SON PROPIEDAD DE KOVATI E.I.R.L.
SU USO Y REPRODUCCION SIN AUTORIZACION PREVIA, ESTAN PROHIBIDOS.

NUMERO DE PLANO ORIGINAL: 15315-2600-46DD-300

FECHA: 07.SET.2026

APROBADO	07.SET.2026	
DISEÑADO POR:	G. MAMANI	FECHA: 07.SET.2026
DIBUJADO POR:	G. MAMANI	FECHA: 07.SET.2026
REVISADO POR:	J. CERRON	FECHA: 07.SET.2026
APROBADO POR:	J. CERRON	FECHA: 07.SET.2026
CLIENTE:	A. COSAITI	FECHA: 07.SET.2026

TECSUP
Arequipa - Perú
PAD B – FASE 1
INGENIERIA DE DETALLE

PLANO: DIAGRAMA UNIFILAR ELÉCTRICO HORNO

ESCALA: S/E

NUMERO DE PLANO: A1-MI09H060-260-70-121

REV.: 0